




POTS

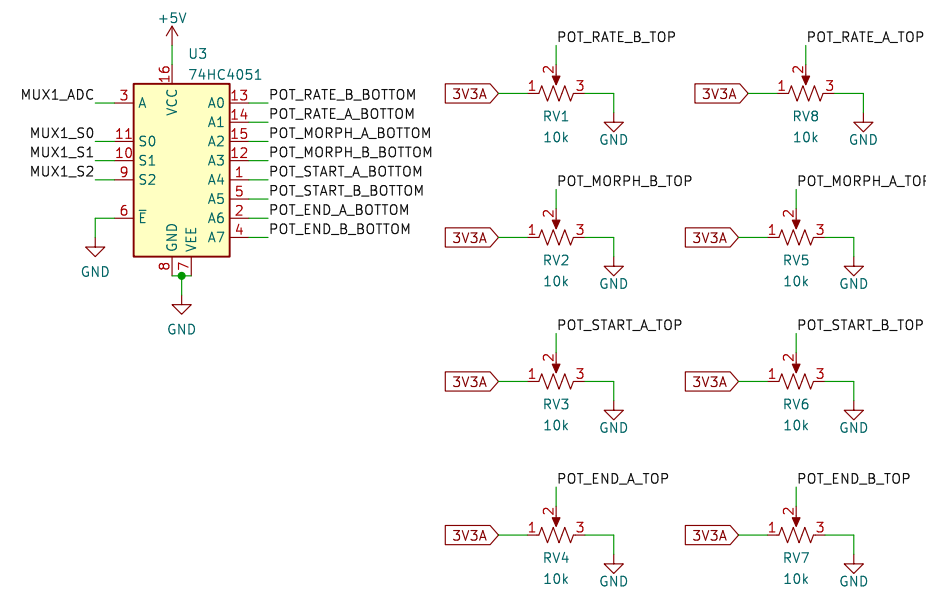


CV OUT

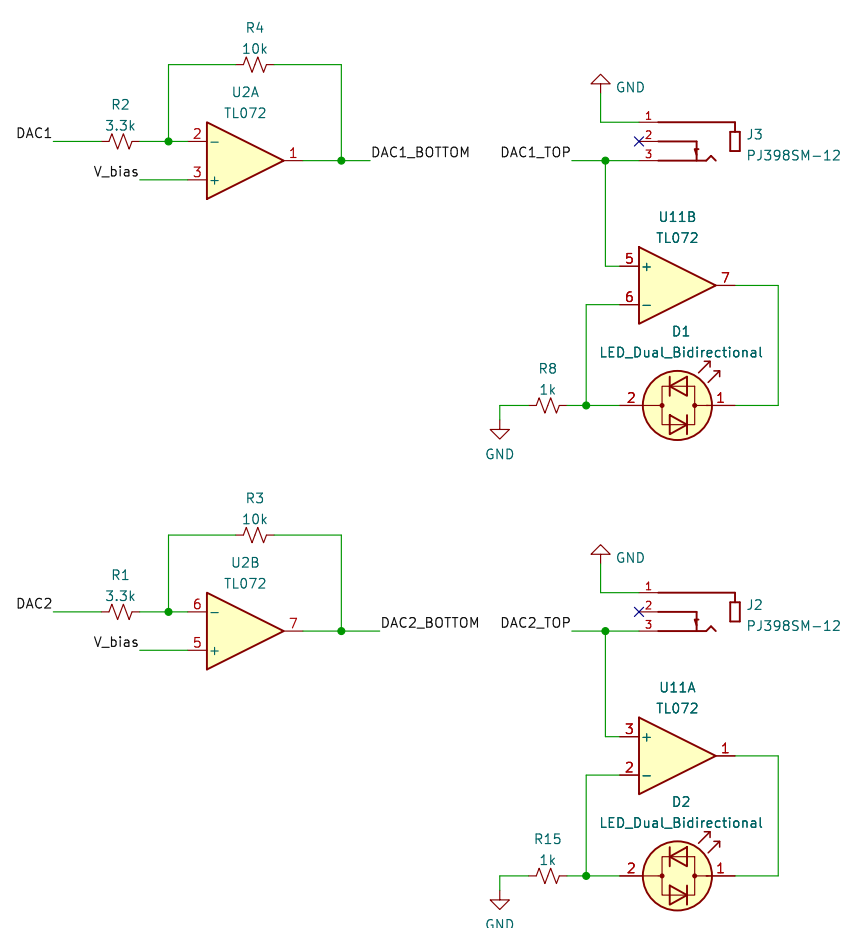


GATE IN

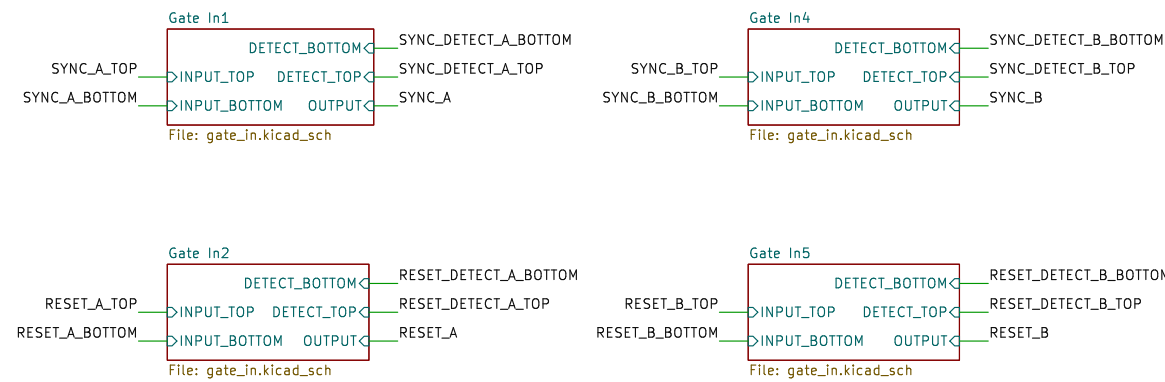


DAISY

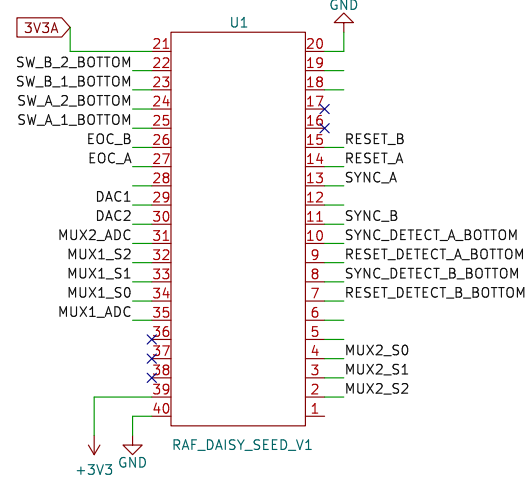


EOC

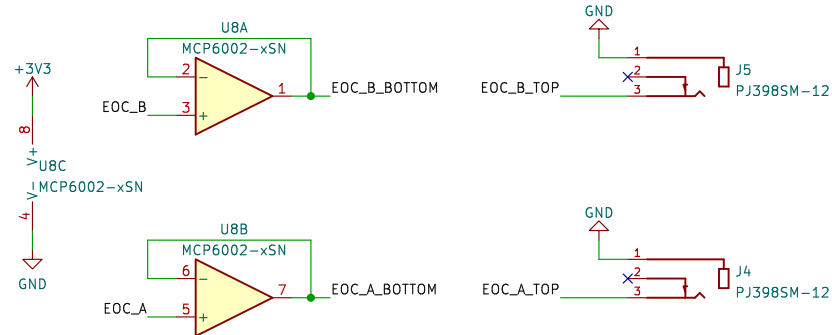

PERIPHERALS

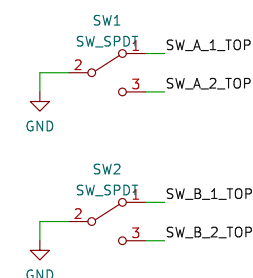

CV IN

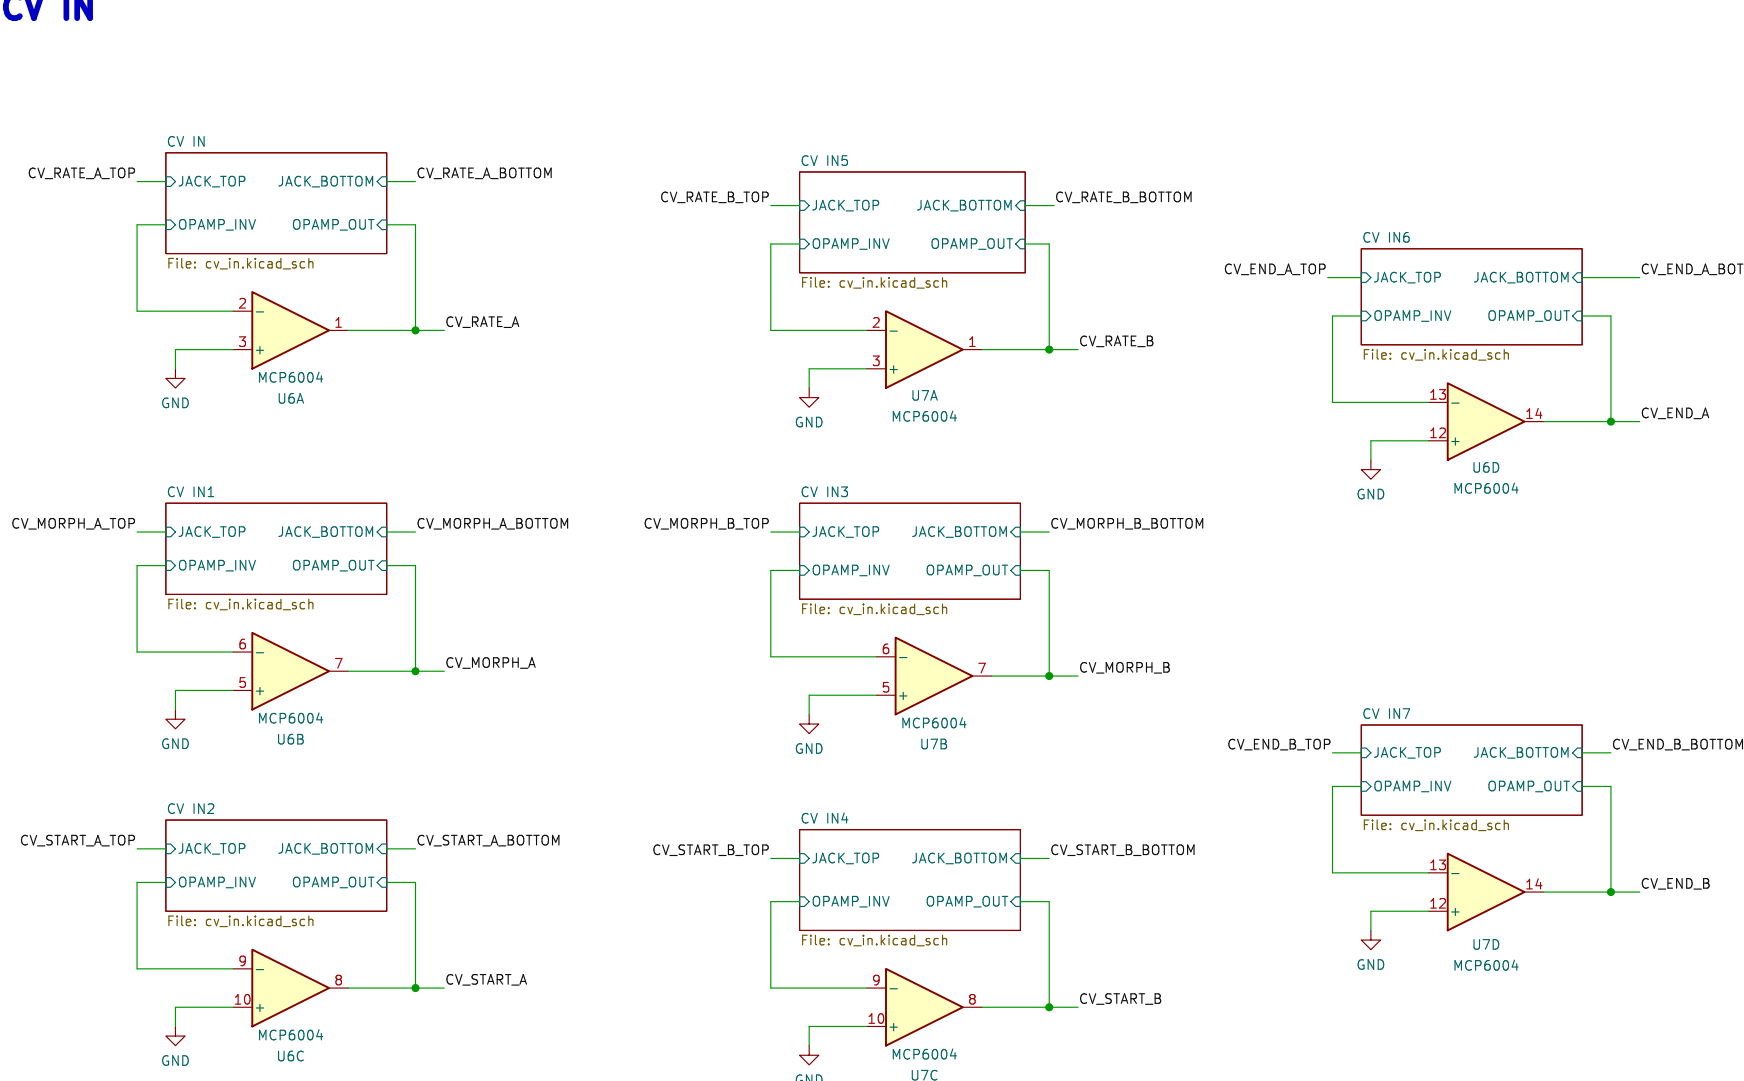

POWER

